
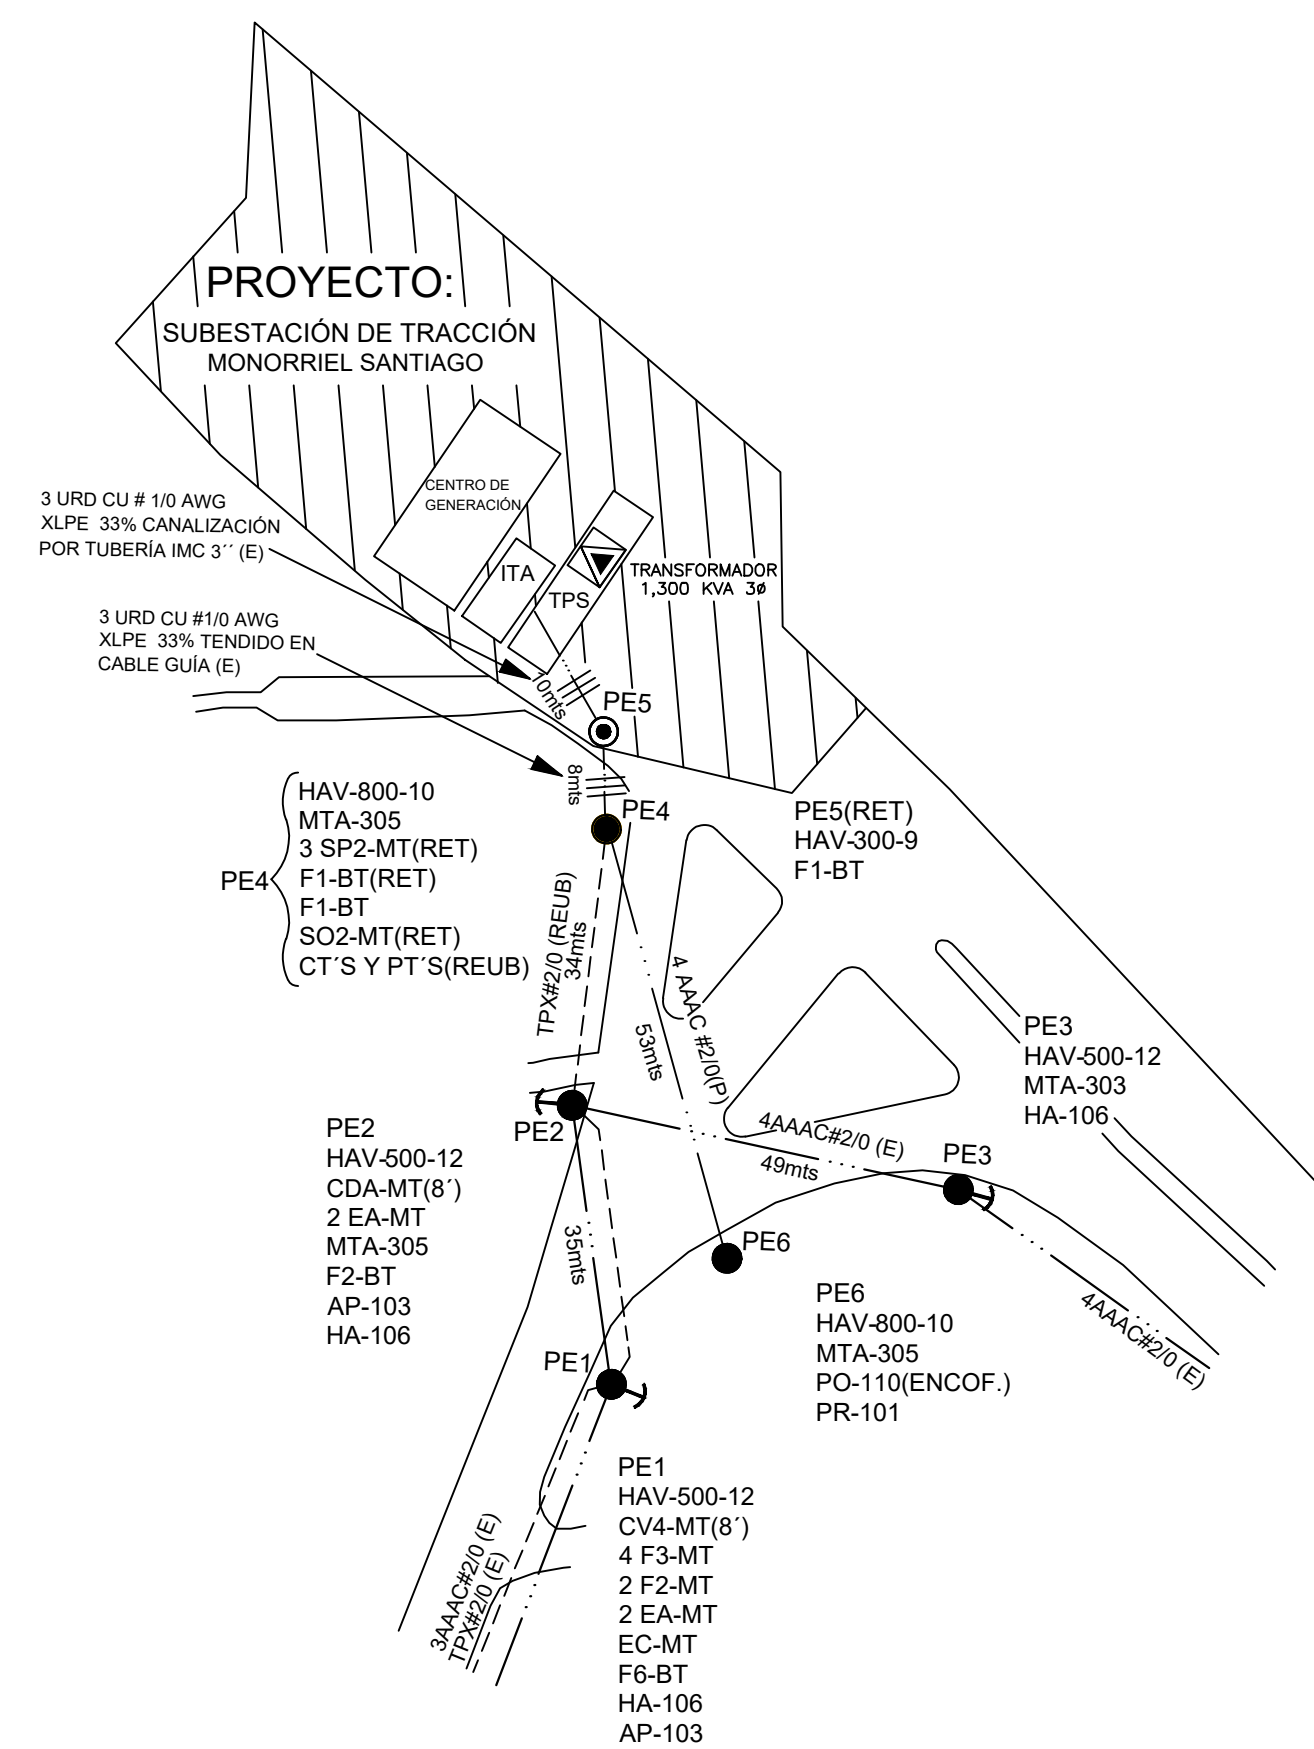


ESCALA: N/A

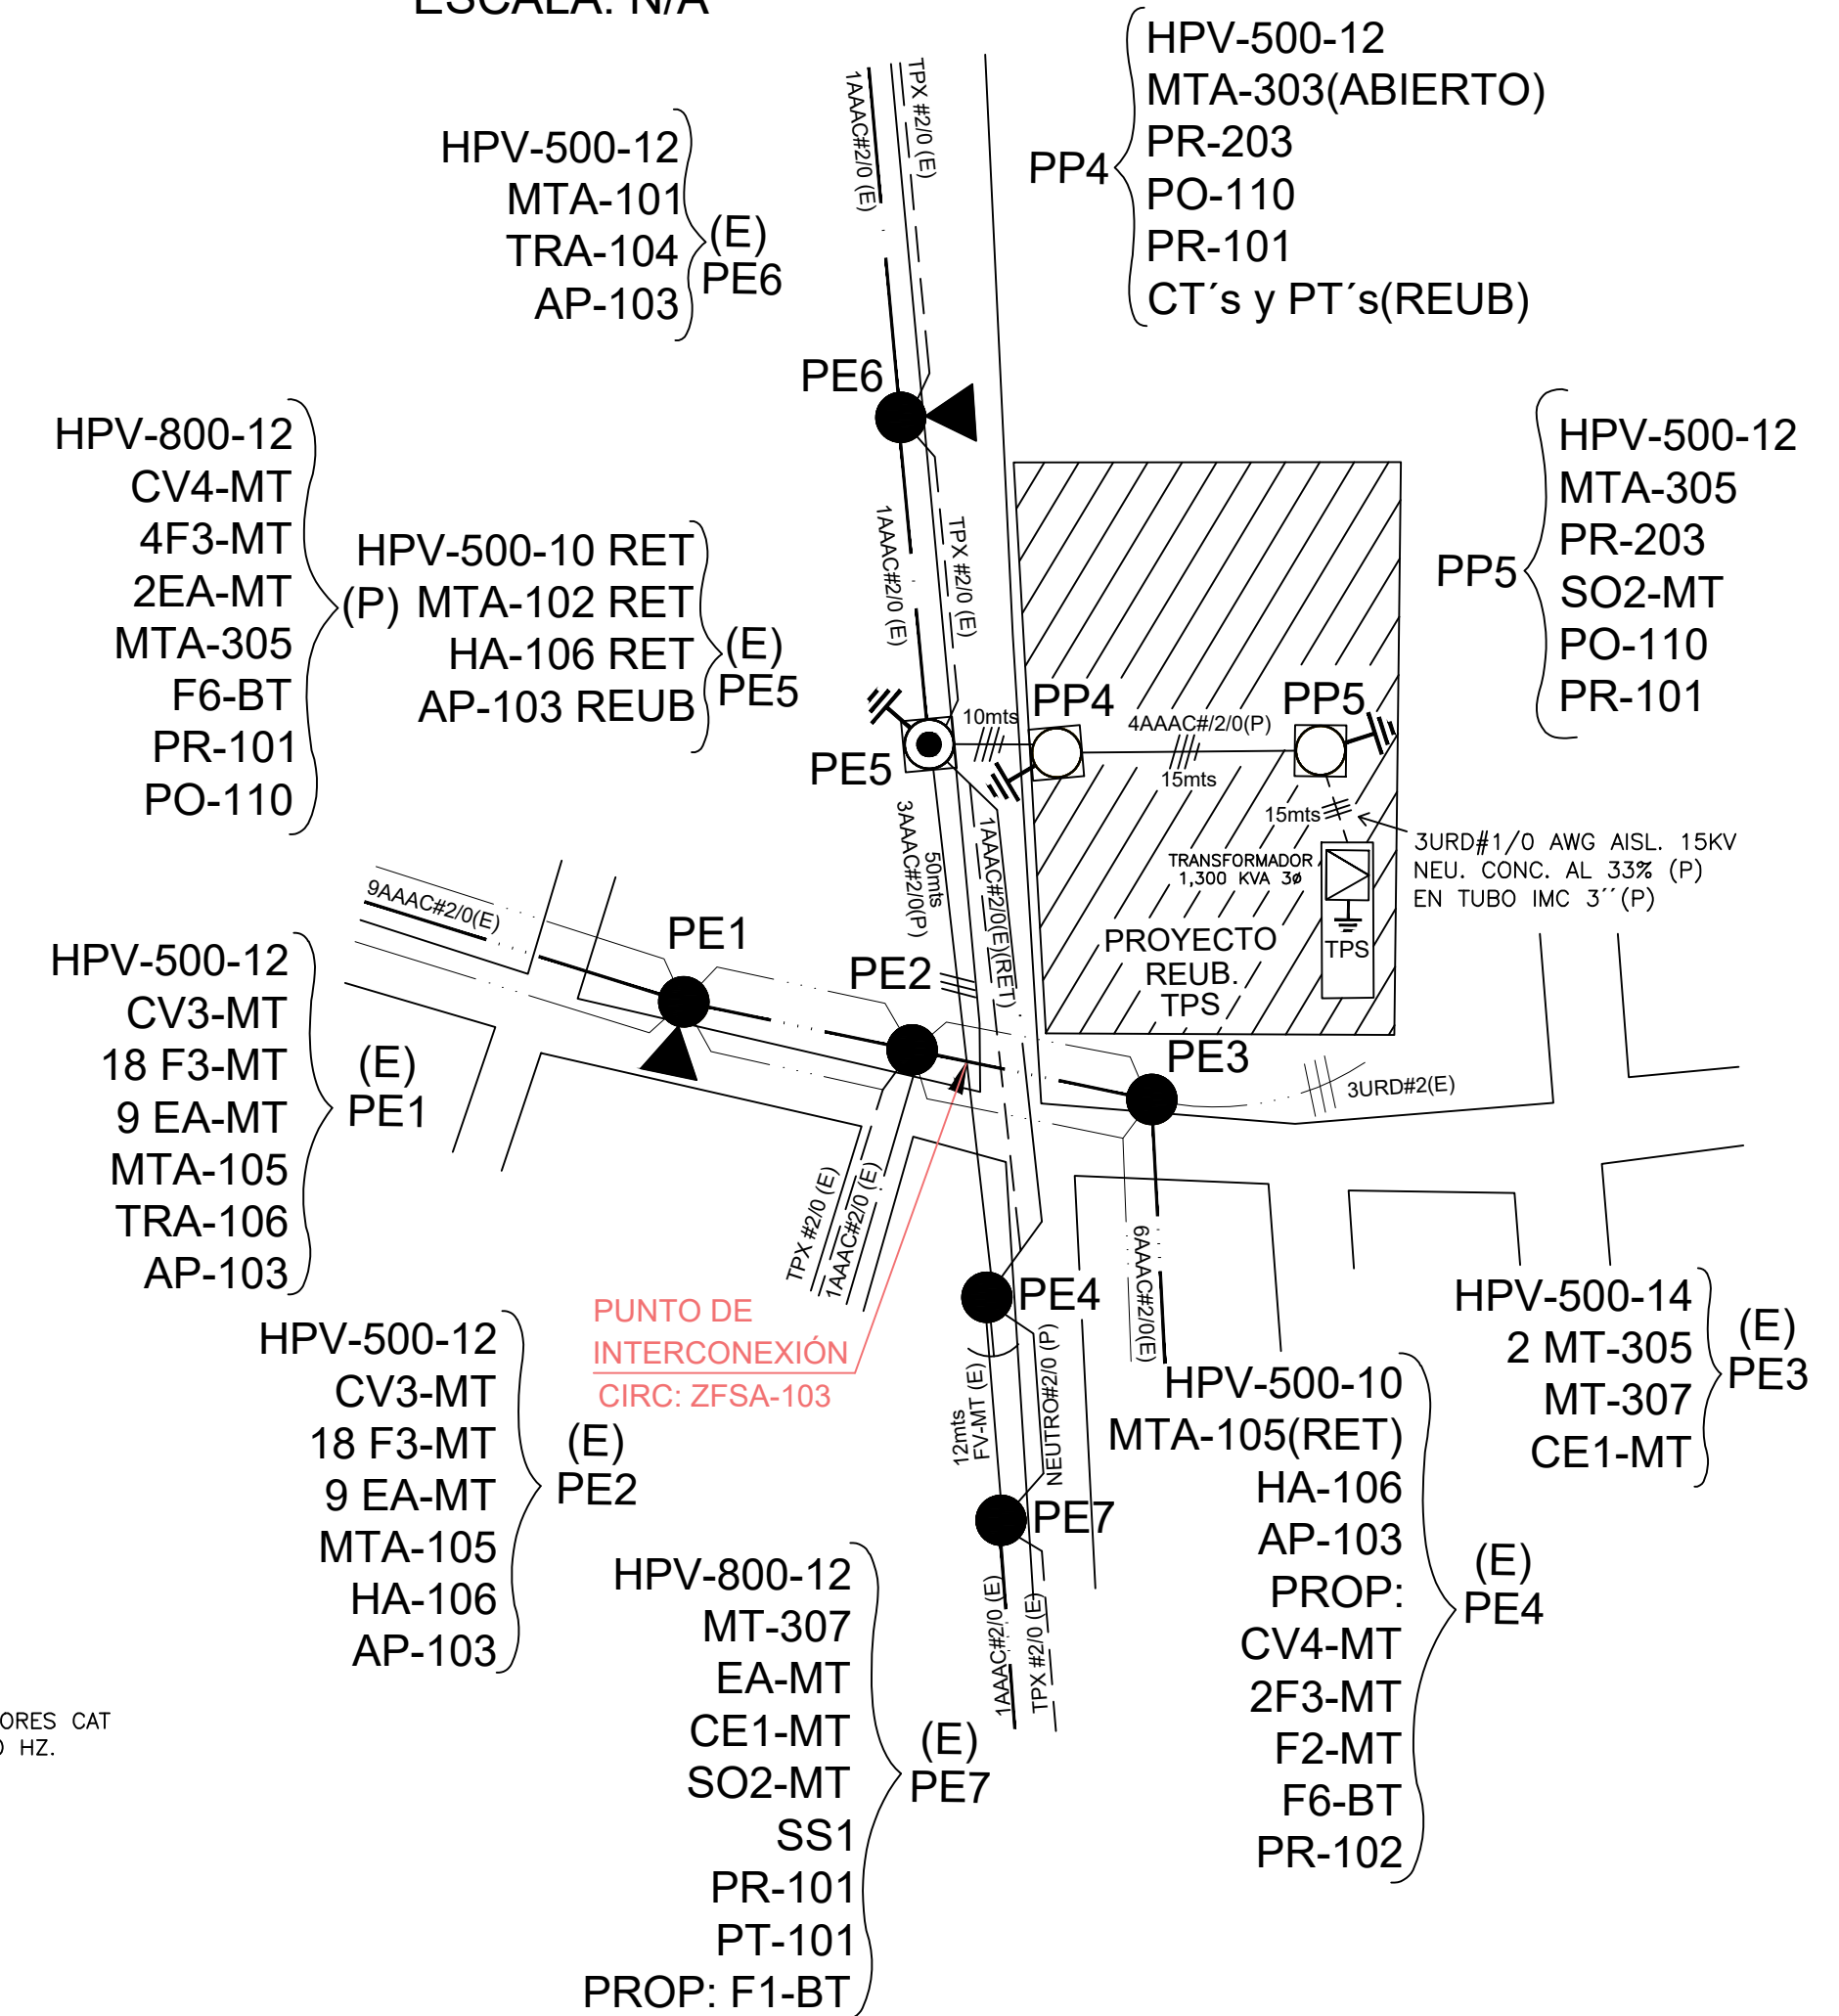

SIMBOLOGÍA	DESCRIPCIÓN
	LÍNEA AEREA TRIFÁSICA CON NEUTRO PRIMARIO PROPUESTO
	LÍNEA AEREA TRIFÁSICA EXISTENTE
	LÍNEA BT - TRIPLEX AEREO EXISTENTE
	POSTE PROPUESTO CIMENTADO
	POSTE EXISTENTE
	POSTE A RETIRAR
	TRANSFORMADOR SUBESTACION PROPUESTO
	GENERADOR DE EMERGENCIAS
	VIENTO EXISTENTE.
	PUESTA A TIERRA.
	PARARRAYO 10KV
	CUT-OUT 100A, 15KV
	MEDIDOR DE ENERGÍA ELÉCTRICA
	TRANSFORMADOR EN DIAGRAMA UNIFILAR
	DISYUNTOR
	TRANSFORMADOR TIPO POSTE EXISTENTE
	TRACTION POWER SUBSTATION (TIPO FURGÓN 40 PIES)
	INTERRUPTOR AUTOMÁTICO DE TRANSFERENCIA (TIPO FURGÓN 20 PIES)
	MV SWITCHGEAR SIEMENS 15 KV
	CT Y PT
	LÍNEA MT SOTERRADA, POR TUBERÍA Y AEREA (URD)
	LÍNEA AEREA MONOFÁSICA EXISTENTE

ESCALA: N/A

[illegible]

MONTE RICO,
SANTIAGO.

COORDENADAS
19.480652, -70.736369

COORDENADAS:
19.480652,
-70.736369

FARMACIA
ICFARMA

PROYECTO
REUB. TPS

ESTACION E3
MONORREIL

ESCUELA BÁSICA
RAFEY

SUBESACIÓN
ZONA FRANCA
SANTIAGO

							FECHA: 26/11/2025	PROYECTO: Reubicacion Subestacion de Traccion Temporal Monorriel de Santiago		
							TIPO: PLANO CONSTRUCCION			
							HOJA: ARCD 24"x36"	NOMBRE DE PLANO: SUBESTACIÓN DE TRACCIÓN MONORRIEL SANTIAGO		
05-12-25	VMI	YFE	PNE	CREACIÓN	REVISIÓN		ESCALA: INDICADA	CÓDIGO DE PLANO:	HOJA	VERSIÓN
29-11-25	YFE	ASI	PNE	CREACIÓN	REVISIÓN			N/P:2164/2026/01/0464	01/01	
05-02-24	YFE	ASI	PNE	CREACIÓN	REVISIÓN					
REV.	FECHA	ELABORADO	VERIFICADO	APROBADO	DESCRIPCIÓN	ESTATUS				

SELO DE APROBACION:



S FRATESA PROJECTS, SRL

PLANOS DE REFERENCIA
1. –
2. –
3. –
4. –
5. –
6. –
7. –
8. –
9. –

OBSERVACIONES:

ESPECIFICACIONES / COMENTARIOS:

- ACOTACIONES EN METROS
- NIVELES EN METROS